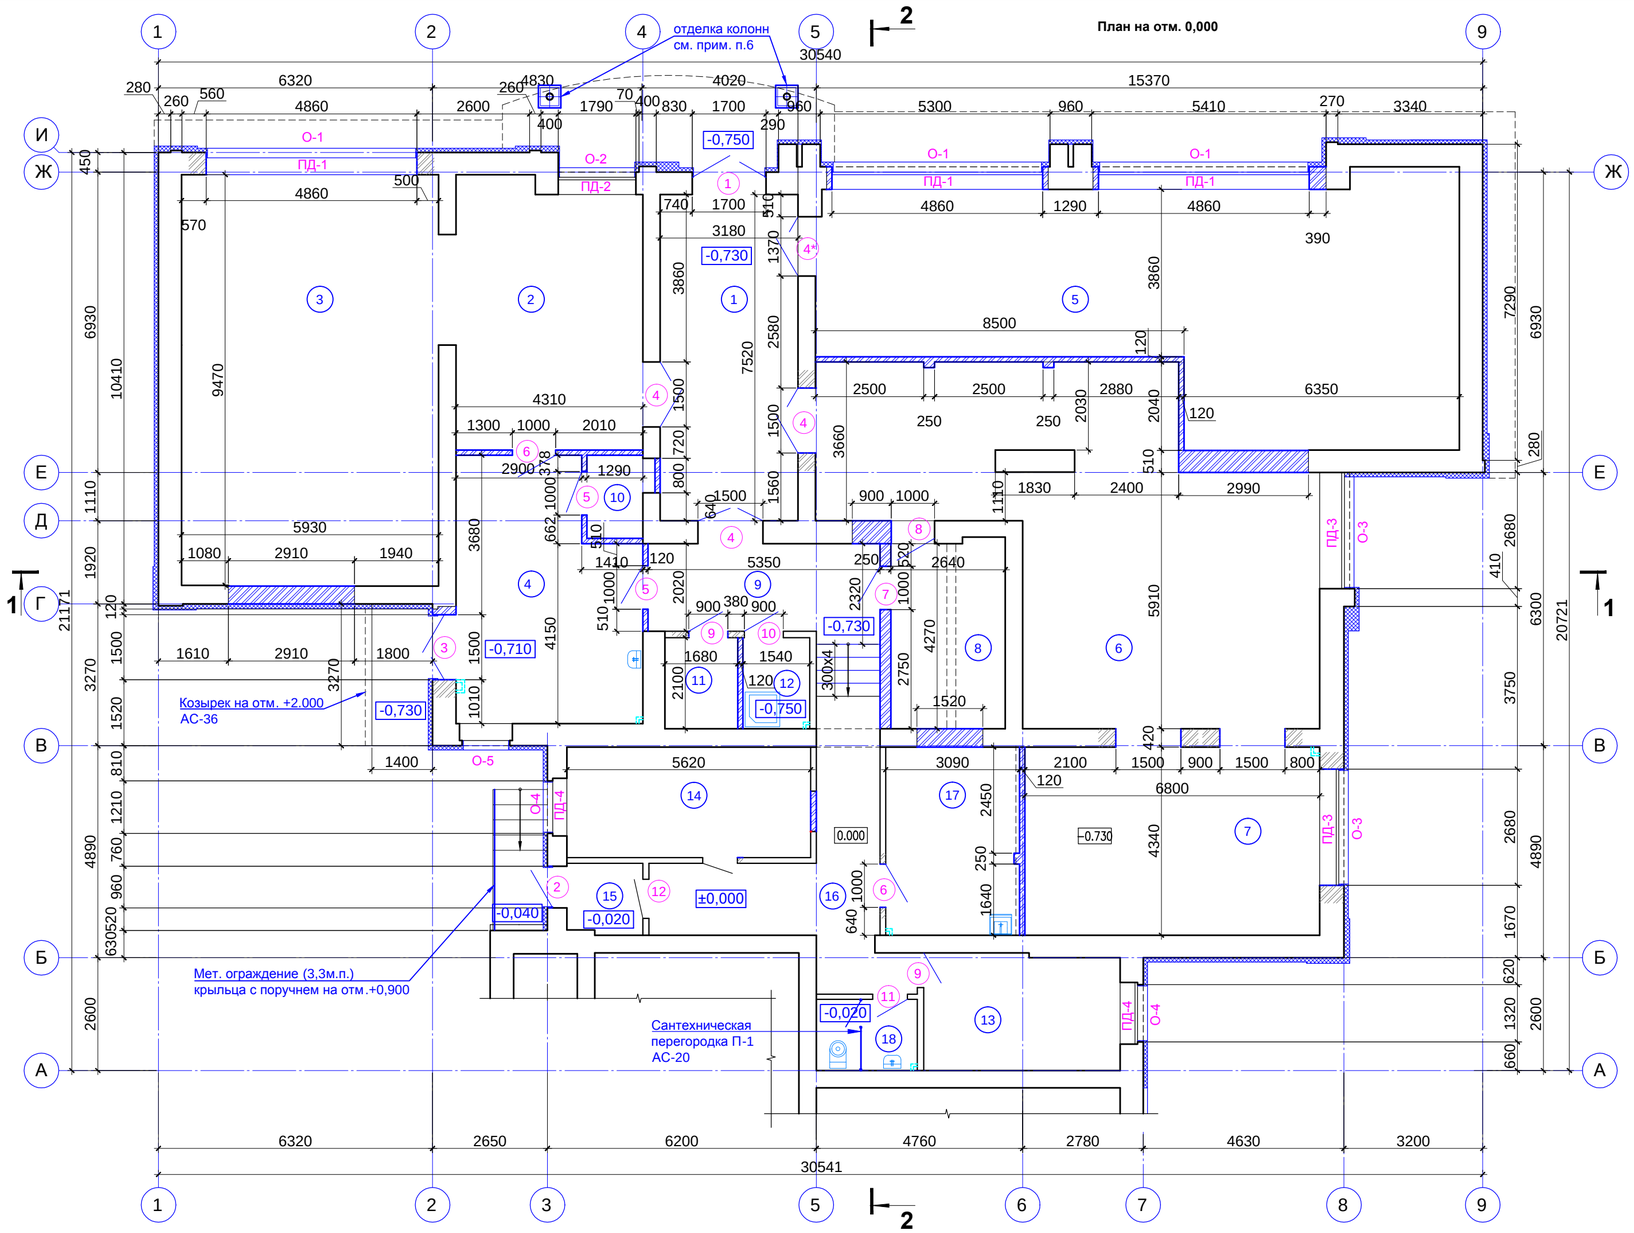

Условные обозначения

- пробивка проемов;
- закладка проемов;
- зашивки ГКЛВ на всю высоту помещения (до уровня подвесного потолка);
- 2 - заполнение дверного проема;
- О-1 - заполнение оконного проема;
- ПД-2 - подоконная доска

Экспликация помещений

Номер помещ.	Помещение	Площадь, м²	Кат. пом.
1	Вестибюль	23,90	
2	Торговый зал	26,20	
3	Торговый зал	56,20	
4	Помещение приемки товаров	23,80	В4
5	Торговый зал	72,20	
6	Торговый зал	65,30	
7	Торговый зал	29,50	
8	Кладовая товаров	11,30	В3
9	Коридор	11,20	
10	Электрощитовая	2,40	В4
11	Кладовая инструмента	3,50	В4
12	Помещение уборочного инвентаря	3,20	Д
13	ИТП	12,00	Д
14	Кабинет администрации	14,30	
15	Тамбур	2,80	
16	Коридор	19,00	
17	Комната приема пищи	13,40	
18	Санузел	3,80	
		394	

1. За относительную отметку 0,000 принята существующая отметка чистого пола административно-бытовой части.
2. Покрытия зон входов должны предусматриваться из материалов с коэффициентом трения μ > 0.40 по СТБ 1751 и должны быть классифицированны по оценочной группе С10-С11, характеризующей степень противоскольжения, У4 - по типу сбросового углубления (изм. 1 РБ СНиП 2.03.13-88).
3. Таблицу марок и материалов стен и перегородок см. лист АС-3 стр.пр.
4. Спецификация элементов заполнения проемов см. лист АС-20 стр.пр.
5. Стены и перегородки выполнить по серии 2.230-1 вып.5 детали 7, 19.
6. Существующие металлические колонны главного входа Ø150мм облицевать фасадными навесными панелями из фиброцемента "под кирпич" по металлическому каркасу АС-46.
7. Отмостку по периметру здания выполнить согласно узла на листе АС-23.
8. Существующая площадка перед главным входом на отм. 0.750 выполнена из бетонной тротуарной плитки. Вдоль осей 3 и 5 ограничена бортом из тротуарной плитки. Нормируемый перепад обеспечен уклонной плоскостью в сторону тротуара.
9. Выполнить ремонт (20%) бетонного крыльца по оси 3 в осях В-Б. Сколы и трещины разделать механическим способом на глубину до 30 мм, очистить и обеспылить их. На подготовленную поверхность трещин нанести кистью состав "ПОЛИМИКС-грунт укрепляющий" и дать ему возможность высохнуть в течении 20-30 минут. Заполнить трещины цем.-песч. р-ром М150.
10. Площадку в помещение разгрузки товара по оси 2 в осях Г-В выполнить согласно узла на листе АС-23.

Изм.	Кол.	Лист	№док.	Подпись	Дата
Разработал		Ефимова			
Проверил		Ефимова			
Н. контр.		Ефимова			
Утвердил		Копать			

11.17-АС

Реконструкция изолированного помещения с инвентарным номером 410/D-205 под административно-торговое помещение непродовольственной группы товаров, расположенного по адресу: г. Волковыск, ул.Ленина, 45-59

Стадия	Лист	Листов
С	14	

План на отм. 0,000

УПРАВЛЕНИЕ строительных проектов ЗАО "АГРОСТРОЙ"

Взам. инв. №

Подп. и дата

Инв. № подл.